


| LEGEND & ABBREVIATIONS |  |                       |
|------------------------|--|-----------------------|
| VP                     |  | Vent Pipe             |
| SP                     |  | Soil Pipe             |
| WP                     |  | Waste Pipe            |
| CDP                    |  | Condensate Drain Pipe |
| RWP                    |  | Rain Water Pipe       |
| PLD                    |  | Planter Drain Pipe    |
| PDP                    |  | Pressure Drain Pipe   |
| CPD                    |  | Car Park Drain        |

| LEGEND & ABBREVIATIONS |                      |
|------------------------|----------------------|
| MH                     | Manhole              |
| GT                     | Gully Trap           |
| FD                     | Floor Drain          |
| CO                     | Clean Out            |
| FCO                    | Floor Clean Out      |
| RWO                    | Rain Water Outlet    |
| PD                     | Planter Drain Outlet |
| TD                     | Trench Drain         |

| LEGEND & ABBREVIATIONS |                 |
|------------------------|-----------------|
| B                      | Basin           |
| BTH                    | Bathtub         |
| DW                     | Dish Washer     |
| FD                     | Floor Drain     |
| SHR                    | Shower          |
| SK                     | Sink            |
| WM                     | Washing Machine |

- NOTE:
- FOR SUMP PITS(SUMP PIT-01 & SUMP PIT-02) AND GREASE INTERCEPTOR, THE ACCESS COVER SHALL BE OF SIZE 1MX1M WITH MEDIUM DUTY DOUBLE SEALED - RECESSED TYPE.
  - FOR SUMP PIT-03 AND OIL INTERCEPTOR, THE ACCESS COVER SHALL BE OF SIZE 1MX1M WITH HEAVY DUTY DOUBLE SEALED - RECESSED TYPE.
  - FOR GULLY TRAP, SAND TRAP AND VALVE PITS OF SUMP PIT-01 AND SUMP PIT-02, THE ACCESS COVER SHALL BE OF SIZE 0.6X0.6M WITH MEDIUM DUTY-RECESSED TYPE.
  - FOR GULLY TRAP, SAND TRAP AND VALVE PITS OF SUMP PIT-03, THE ACCESS COVER SHALL BE OF SIZE 0.6X0.6M WITH HEAVY DUTY DOUBLE SEALED - RECESSED TYPE.

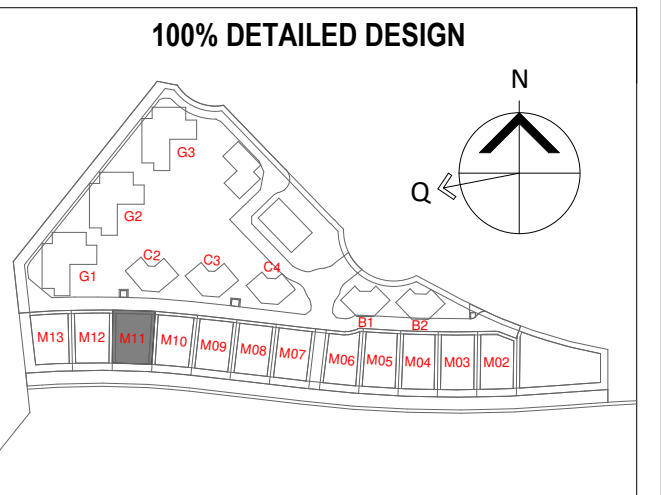

| Rev. | Description                        | Date       | Check | Appr |
|------|------------------------------------|------------|-------|------|
| R03  | 100% DETAILED DESIGN SUBMISSION    | 24-12-2025 | M.I.  | B.R. |
| R02  | 50% DETAILED DESIGN SUBMISSION     | 15-11-2025 | M.I.  | B.J. |
| R01  | 100% SCHEMATIC DESIGN RESUBMISSION | 26-10-2025 | M.K.  | AA   |
| P00  | 100% SCHEMATIC DESIGN SUBMISSION   | 26-09-2025 | M.K.  | AA   |

**GENERAL NOTES:**

- Any discrepancies in the figured dimension are to be reported immediately to the architect.
- Contractors must check and verify all dimensions on site before commencement of work.
- All dimensions are in millimeters.
- All levels shown on drawings are finished floor levels unless specified otherwise.
- This drawing is a copyright and property of the Architect, is not to be produced, copied, handed over to a third party or used for any other purpose other than for which it is intended.
- The construction manager/contractor must check all dimensions and details and be responsible for the same. Any discrepancy shall be brought to the notice of the Architect.
- This drawing is to be read and not scaled.
- This drawing shall be read in conjunction with all relevant Architectural, Structural, and Services drawings. Any discrepancy noticed shall be brought to the attention of the Consultants within responsible time of receipt of this drawings, but always prior to procurement / execution of works.

**MASTER DEVELOPER**

مدينة دبي الطبية  
Dubai Healthcare City

**CLIENT OPERATOR**

مركز لوف أوف حياة  
MAG OF LIFE  
MAG OF LIFE FZ-LLC

**MAIN CONTRACTOR**

CECEP

**LEAD & DESIGN CONSULTANT**

RSP ARCHITECTS PLANNERS & ENGINEERS (PTE) LTD  
(Dubai Branch)  
P.O. Box 191780, Dubai, U.A.E.  
Tel: +971 4 4418 456  
Fax: +971 4 4418 274  
www.rsp-design.com

**PROJECT**

**KETURAH RESORT**  
PLOT M11-EARTH MANSION (B+G+2+ROOF)

**OWNER**

**MAG OF LIFE FZ-L.L.C.**

**PLOT NO:** PLOT M11 (3262995) **BLOCK:** DHC-PHASE 2, AL JADAF

**SHEET INFORMATION**


|               |                      |
|---------------|----------------------|
| PROJECT NBR.  | RST                  |
| PROJECT PHASE | 100% DETAILED DESIGN |
| DISCIPLINE    | DRAINAGE             |
| SECTOR        |                      |
| BUILDING      | EV4                  |
| DESIGNED      | M.K.                 |
| DRAWN         | A.R.                 |
| CHECKED       | M.I.                 |
| APPROVED      | B.R.                 |
| DATE          | 24-12-2025           |
| SCALE         | 1:100                |

**SHEET TITLE**

**EV4**  
**PLOT M11-BASEMENT FLOOR**  
**PLAN-DRAINAGE**

**SHEET NUMBER**

**RST-RSP-M11-EV4-B01-DRW-PDR-220001 P03**

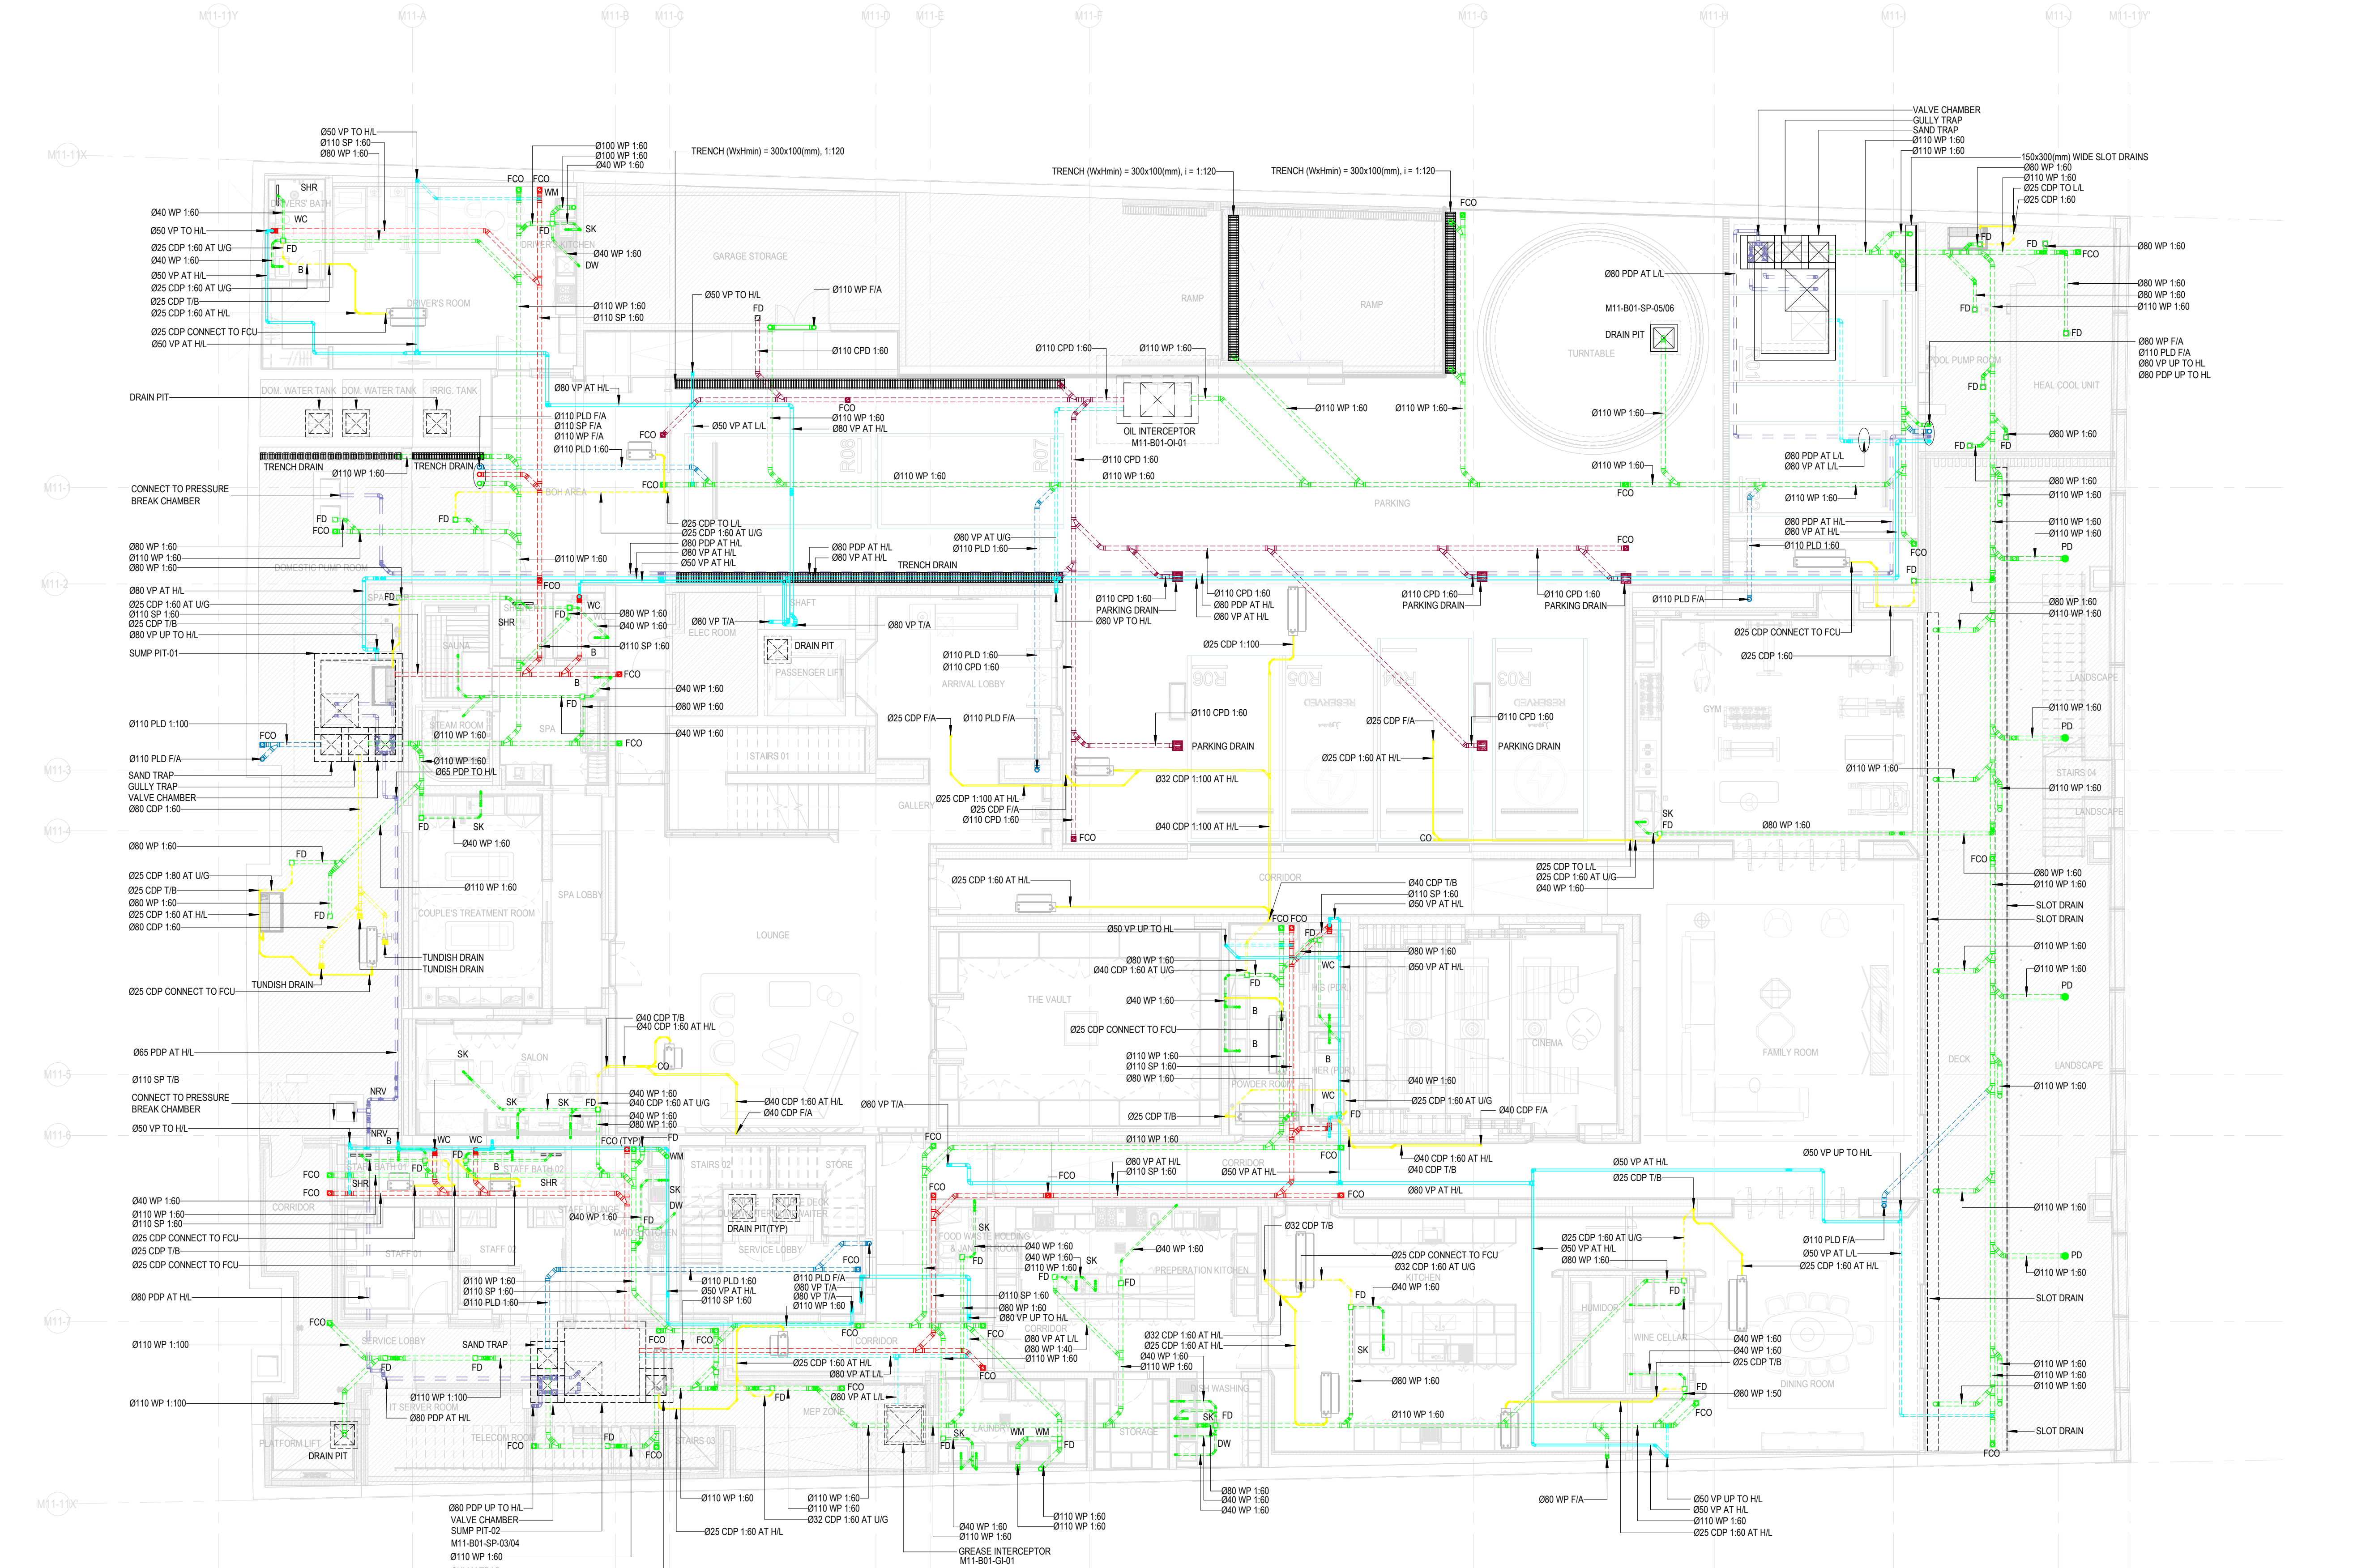

**1 PLOT M11-BASEMENT FLOOR PLAN-DRAINAGE**  
1:100

12/25/2025 12:35:44 AM