


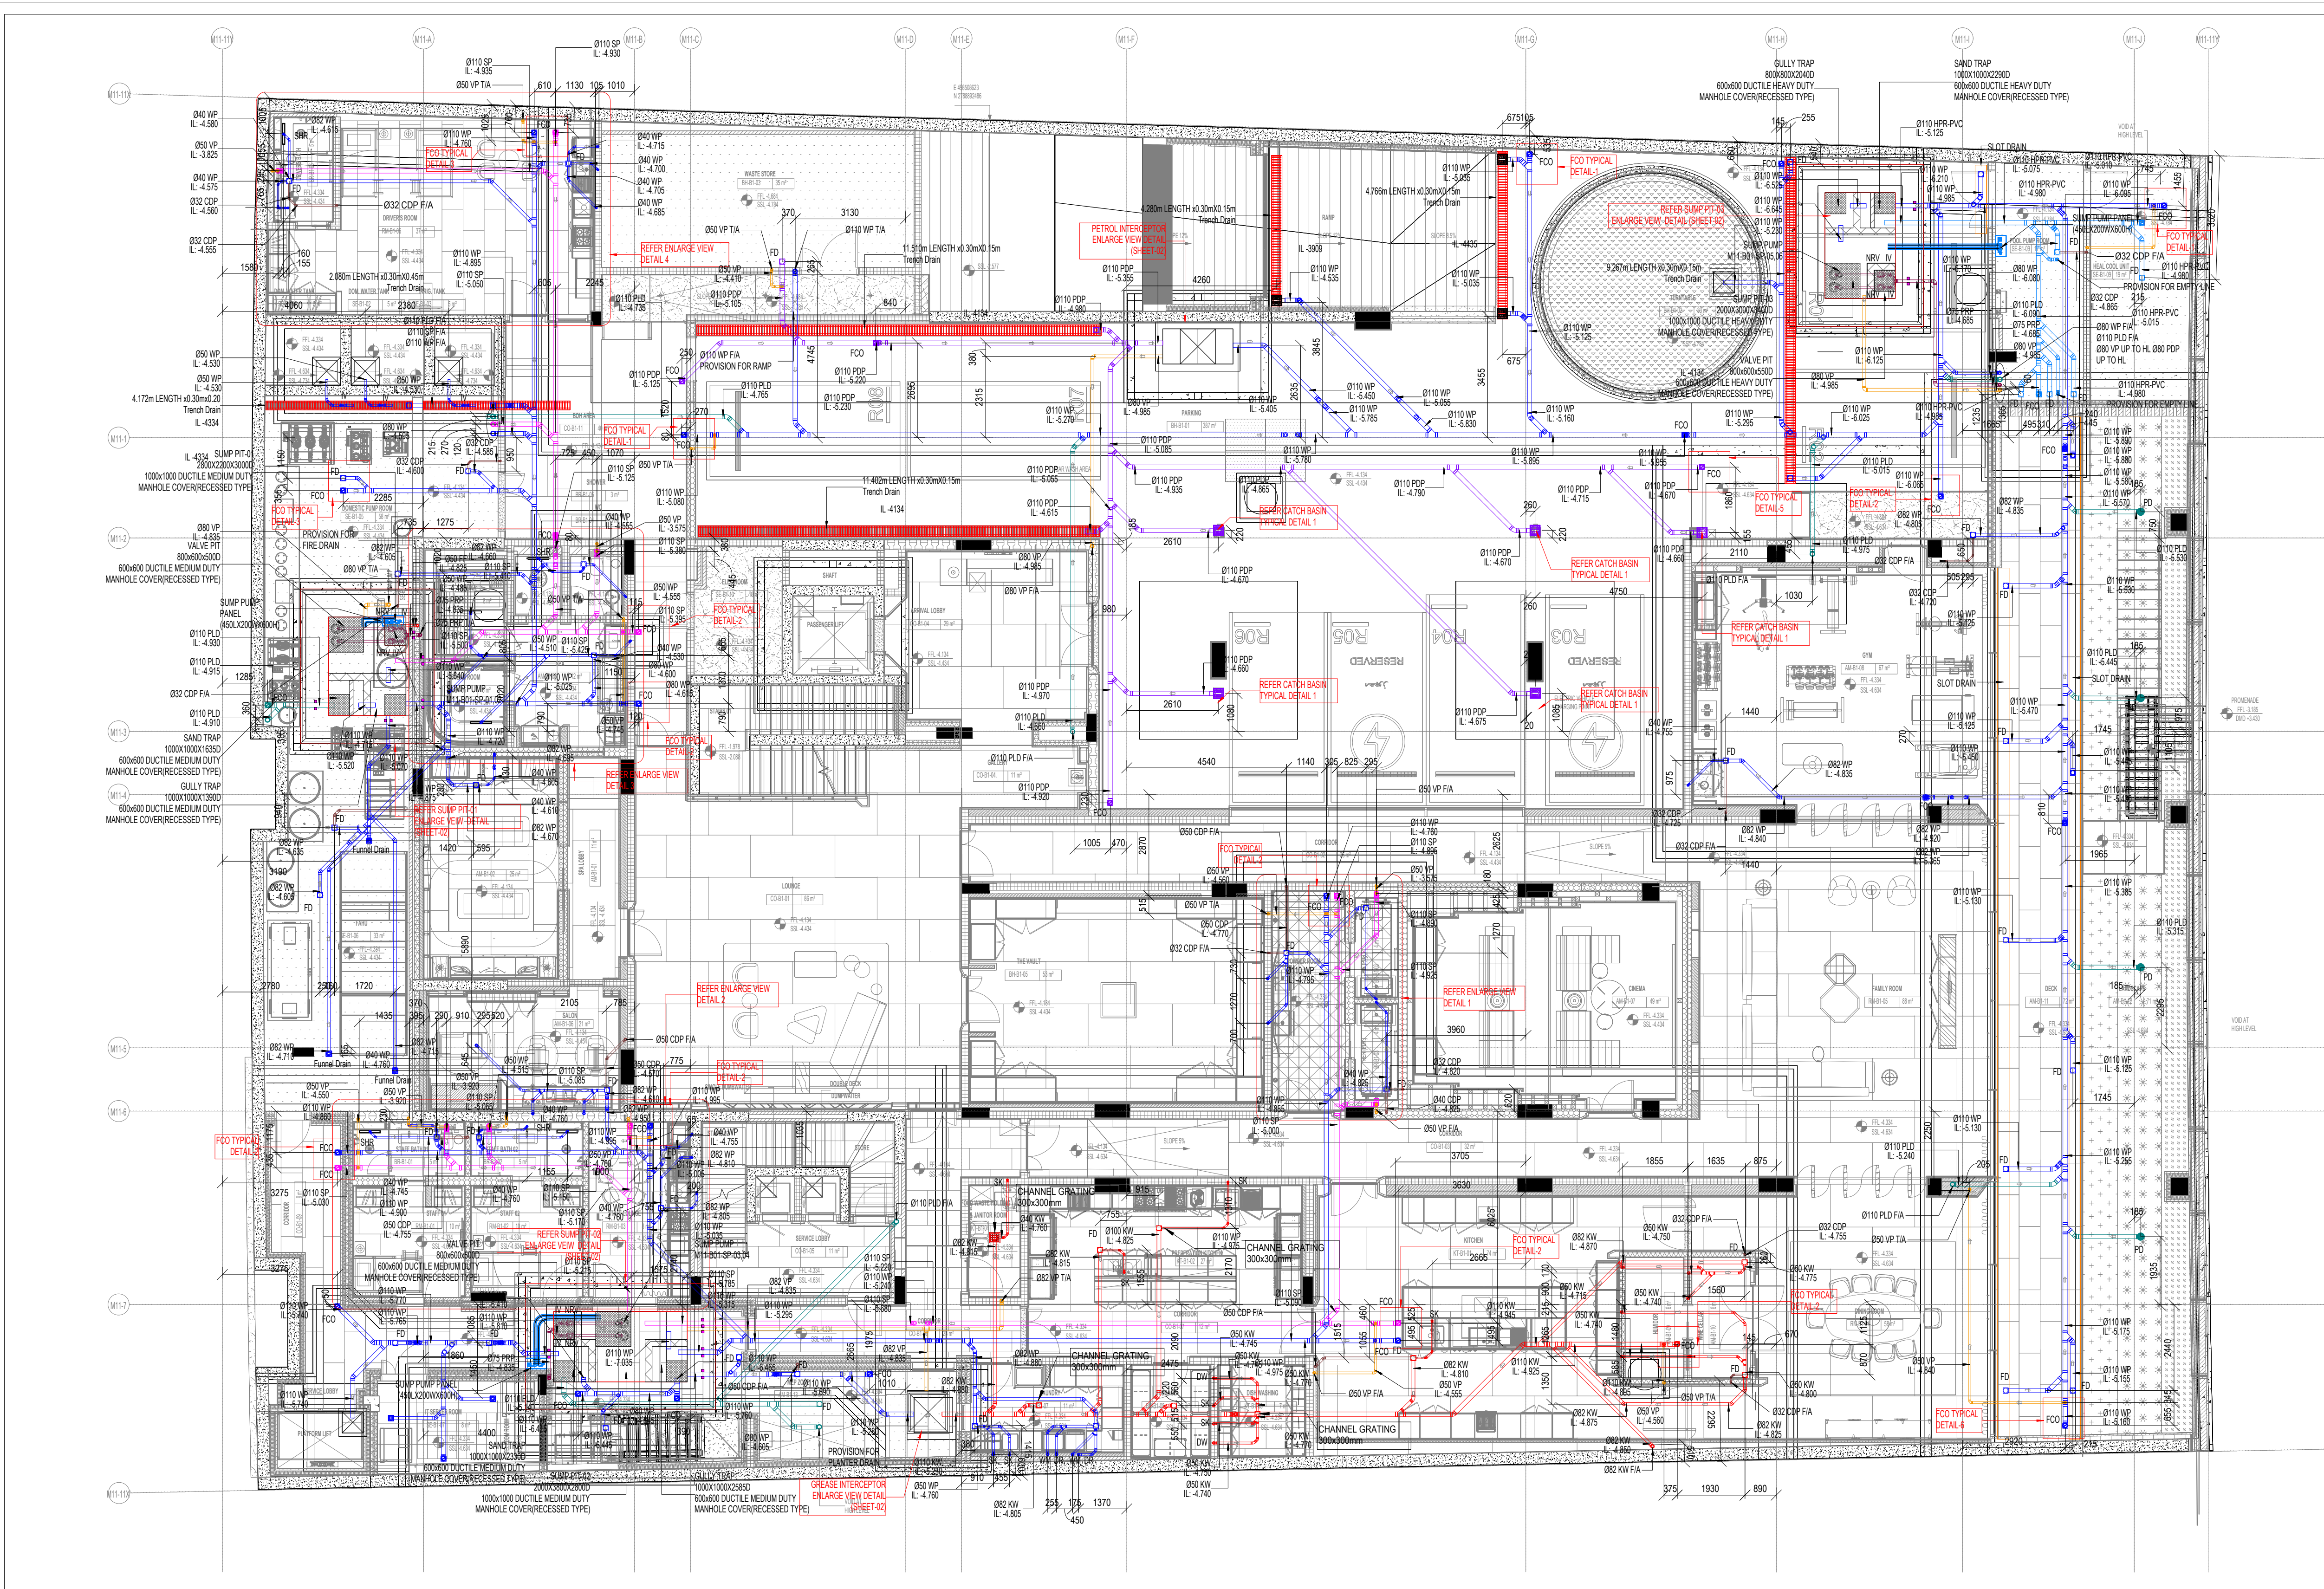


1 M11-BASEMENT FLOOR PLAN-DRAINAGE LAYOUT
1 : 100

PLUMBING LEGEND	
SYMBOL	DESCRIPTION
	SOIL PIPE-uPVC
	WASTE PIPE-uPVC
	VENT PIPE-uPVC
	RAINWATER PIPE-uPVC
	KITCHEN WASTE PIPE-HDPE

	CONDENSATE DRAIN PIPE-uPVC
	PUMP DISCHARGE PIPE-PVC
	PLANTER DRAIN PIPE-uPVC
	PARKING DRAIN PIPE-uPVC
	HEAT COOL DRAIN HPR-PVC
	FLOOR DRAIN
	FLOOR CLEAN OUT

	GULLY TRAP
	SAND TRAP
	SUMP PIT
	CHANNEL GRATING
	PUDDLE FLANGE
	FROM ABOVE
	TO ABOVE

TA	TO ABOVE
FB	FROM ABOVE
TB	TO BELOW

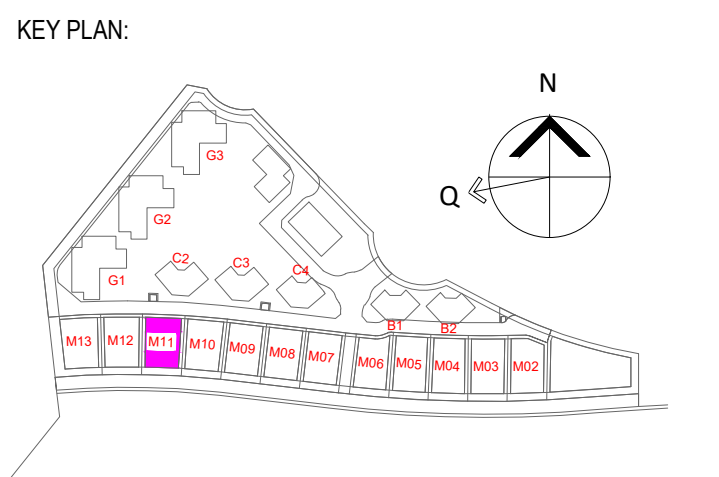

Approval Stamp

Notes:
1. ALL DIMENSIONS AND LEVELS ARE IN MILLIMETERS
UNLESS OTHERWISE NOTED.

REFERENCE	DRAWING NO.	DRAWING TITLE	REV
RST-RSP-M11-EV4-B01-DRW-ARC-220001		PLOT M11-BASEMENT FLOOR PLAN	00
RST-RSP-M11-EV4-B01-DRW-STR-220001		FOUNDATION LEVEL GENERAL ARRANGEMENT	00
RST-RSP-M11-EV4-B01-DRW-GEN-220001		OVERALL FLOOR PLAN - M11 EV AT BASEMENT FLOOR	P03
RST-RSP-M11-EV4-B01-DRW-LAN-110001		BASEMENT FLOOR - GENERAL ARRANGEMENT PLAN	00
RST-RSP-M11-EV4-B01-DRW-PDR-220001		PLOT M11-BASEMENT FLOOR PLAN-DRAINAGE	P03

CITIC REVIEW STATUS:	
REVIEWER	SIGN
ARCHITECT	
STRUCTURE	
ELECTRICAL	
MECHANICAL	

01	23-07-2026	REVISED AS PER COMMENTS	SS
00	05-06-2026	ISSUED FOR APPROVAL	SS
REV.NO.	DATE	DESCRIPTION	APPROV BY

Project:

KETURAH RESORT

Client:

Dubai Healthcare City

Developer:

MAG OF LIFE FZ-LLC

Design Consultant:

Lead Consultant / Supervision Engineer:
RSP ARCHITECTS PLANNERS & ENGINEERS (PTE) LTD
P.O. Box 81718, Dubai, UAE
Tel: +971 4 418 18 42
Fax: +971 4 418 18 24
www.rsp.ae

Main Contractor:

中信建设 (阿联酋) 有限责任公司
CITIC MIDDLE EAST CONTRACTING L.L.C.

M.E.P. Contractor:

中信建设 (阿联酋) 有限责任公司
CITIC MIDDLE EAST CONTRACTING L.L.C.

Building Reference:

M11

Drawing Title:
EV4
M11 BASEMENT FLOOR PLAN
DRAINAGE LAYOUT

Prepared	Noor	Checked	Siva
Drawn	Noor	Approved	Ahmed
Scale	1:100	Date	23/07/26
Original Size	A1	Project No.	

RST-CIT-M11-EV4-B01-DRW-PDR-220001