
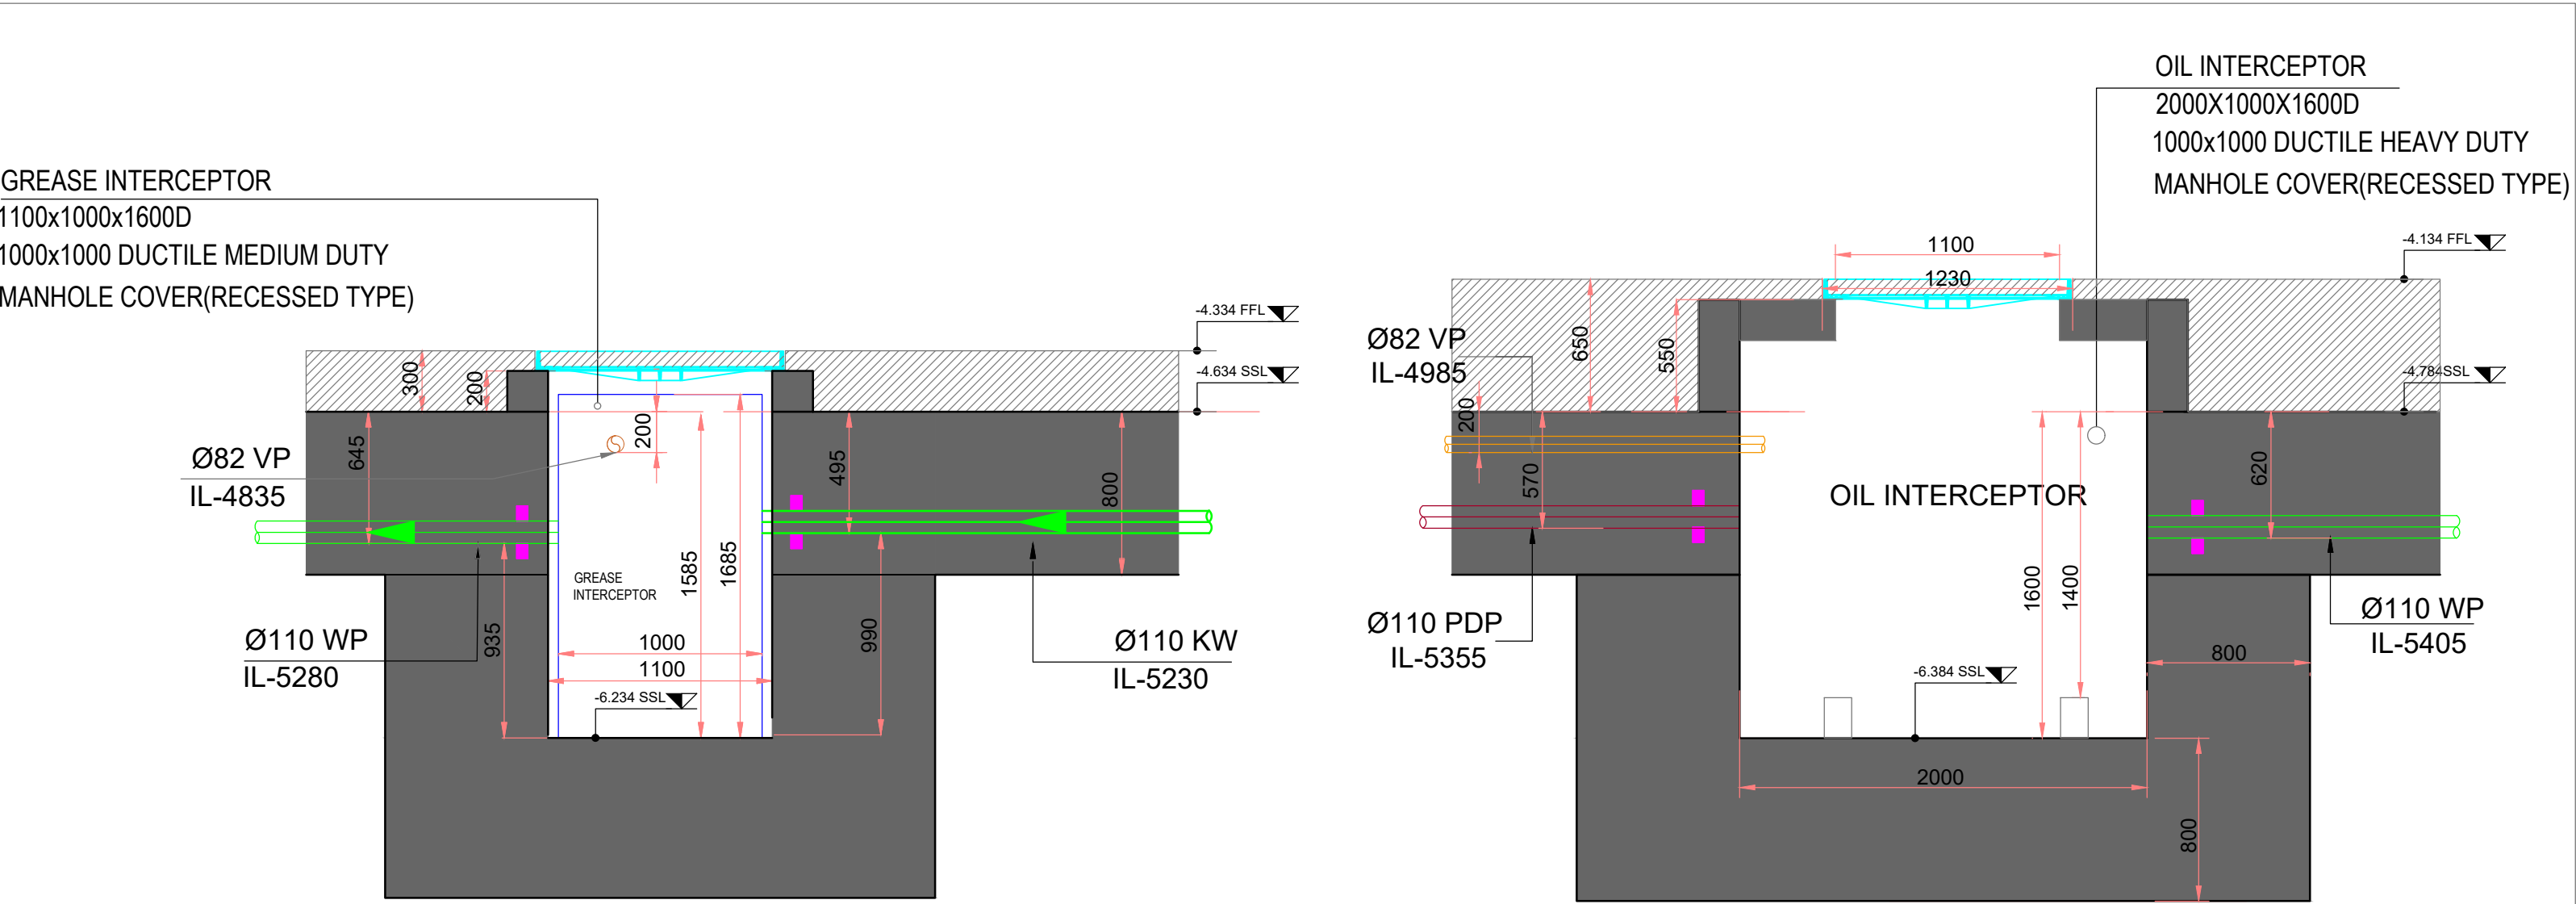
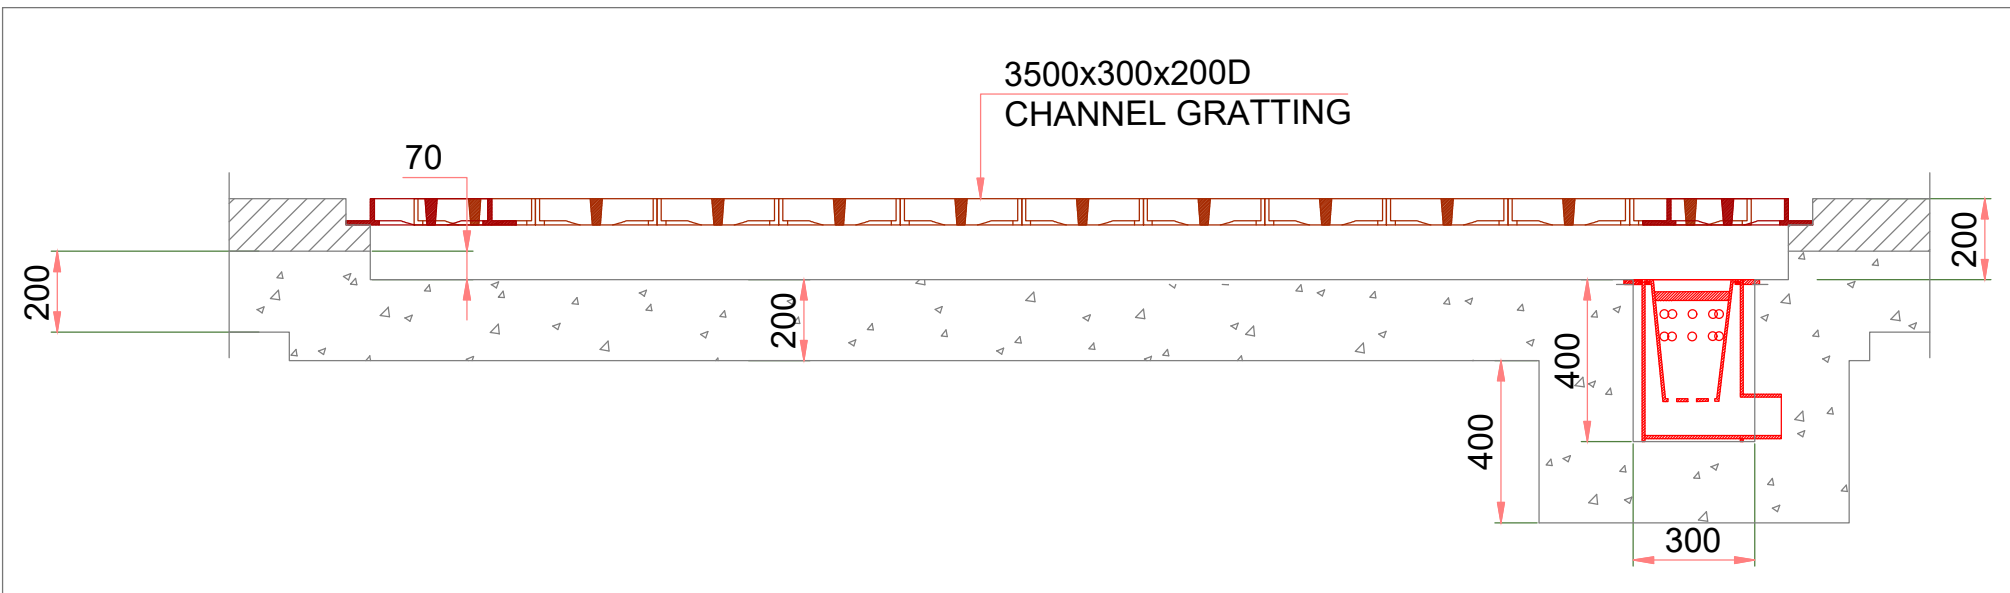
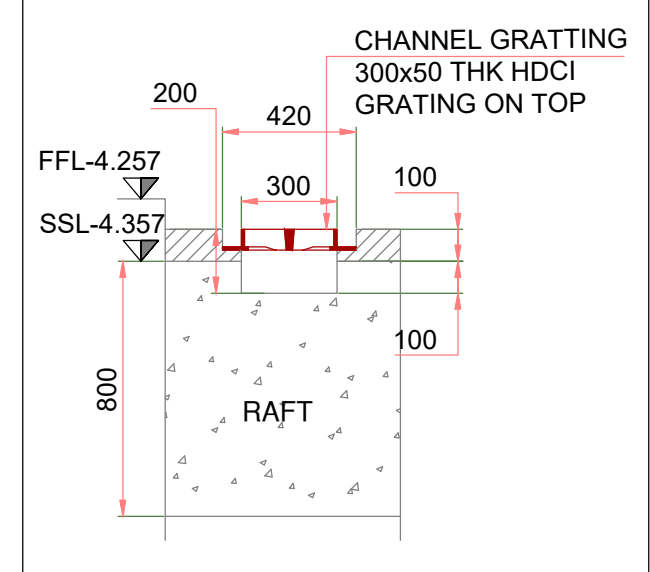
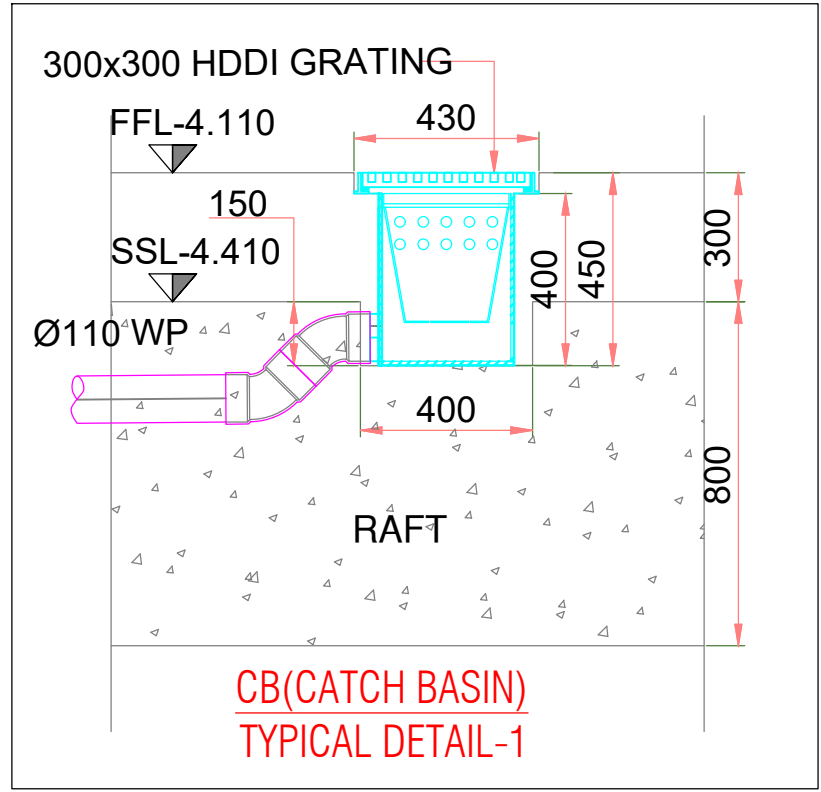
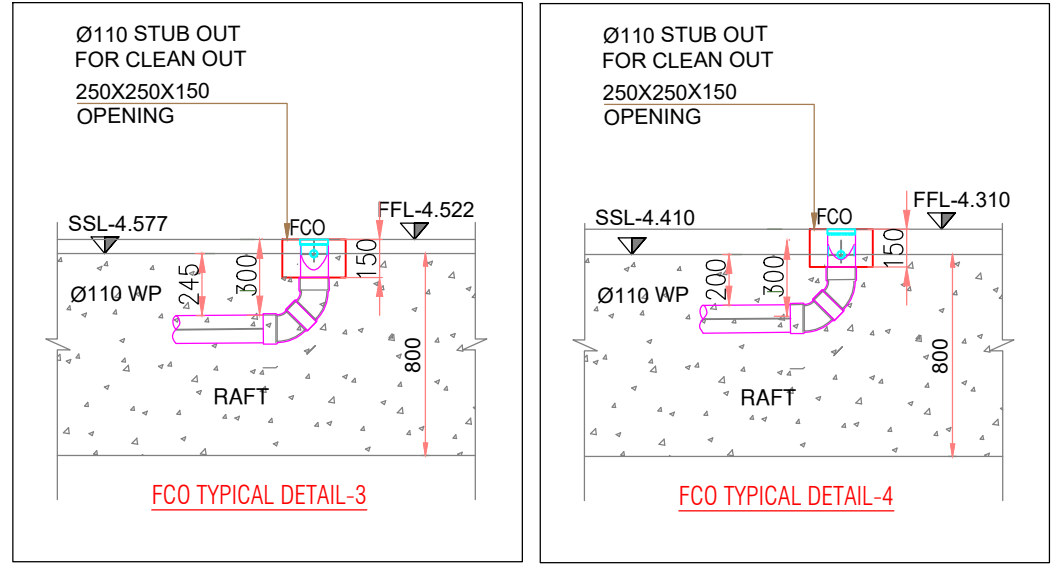
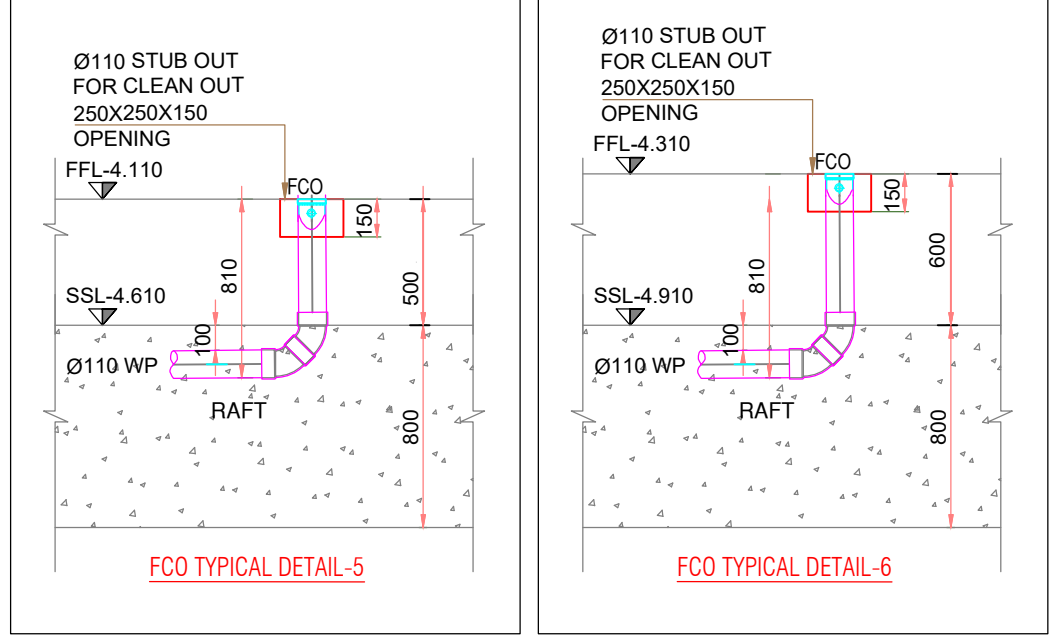
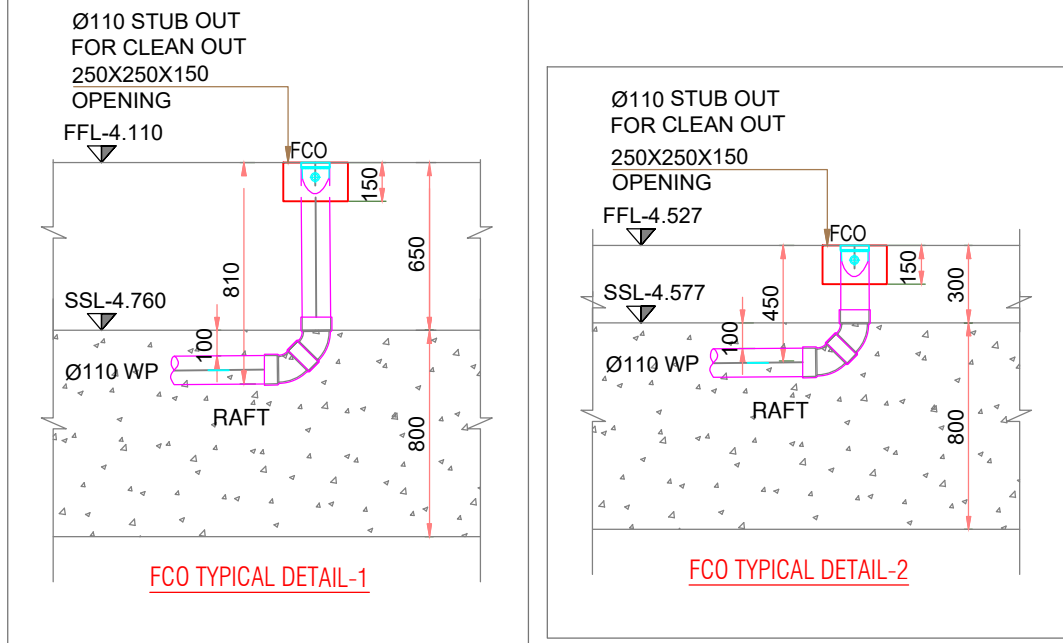
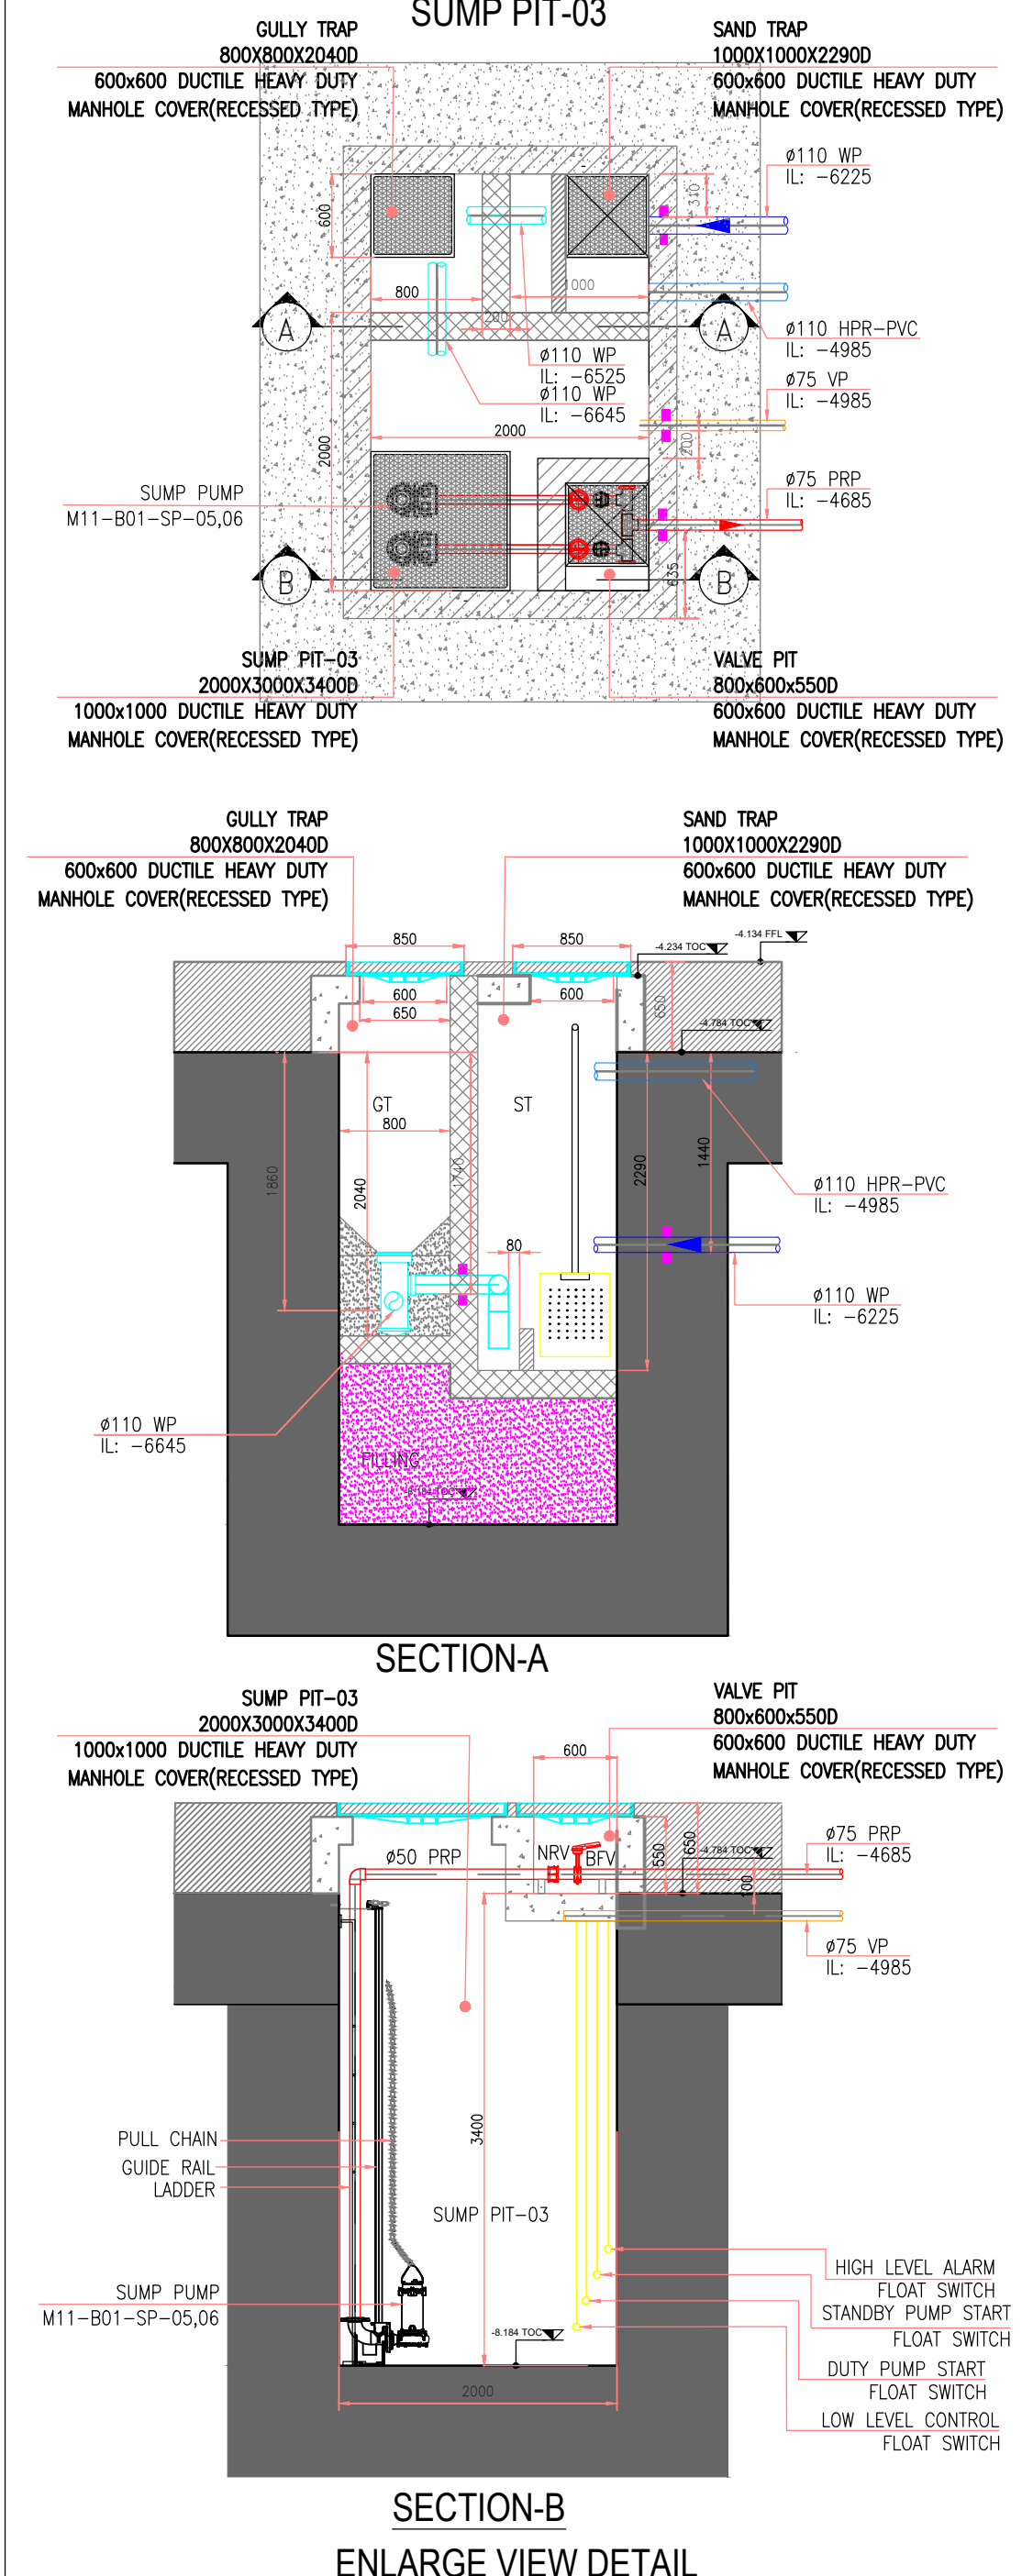
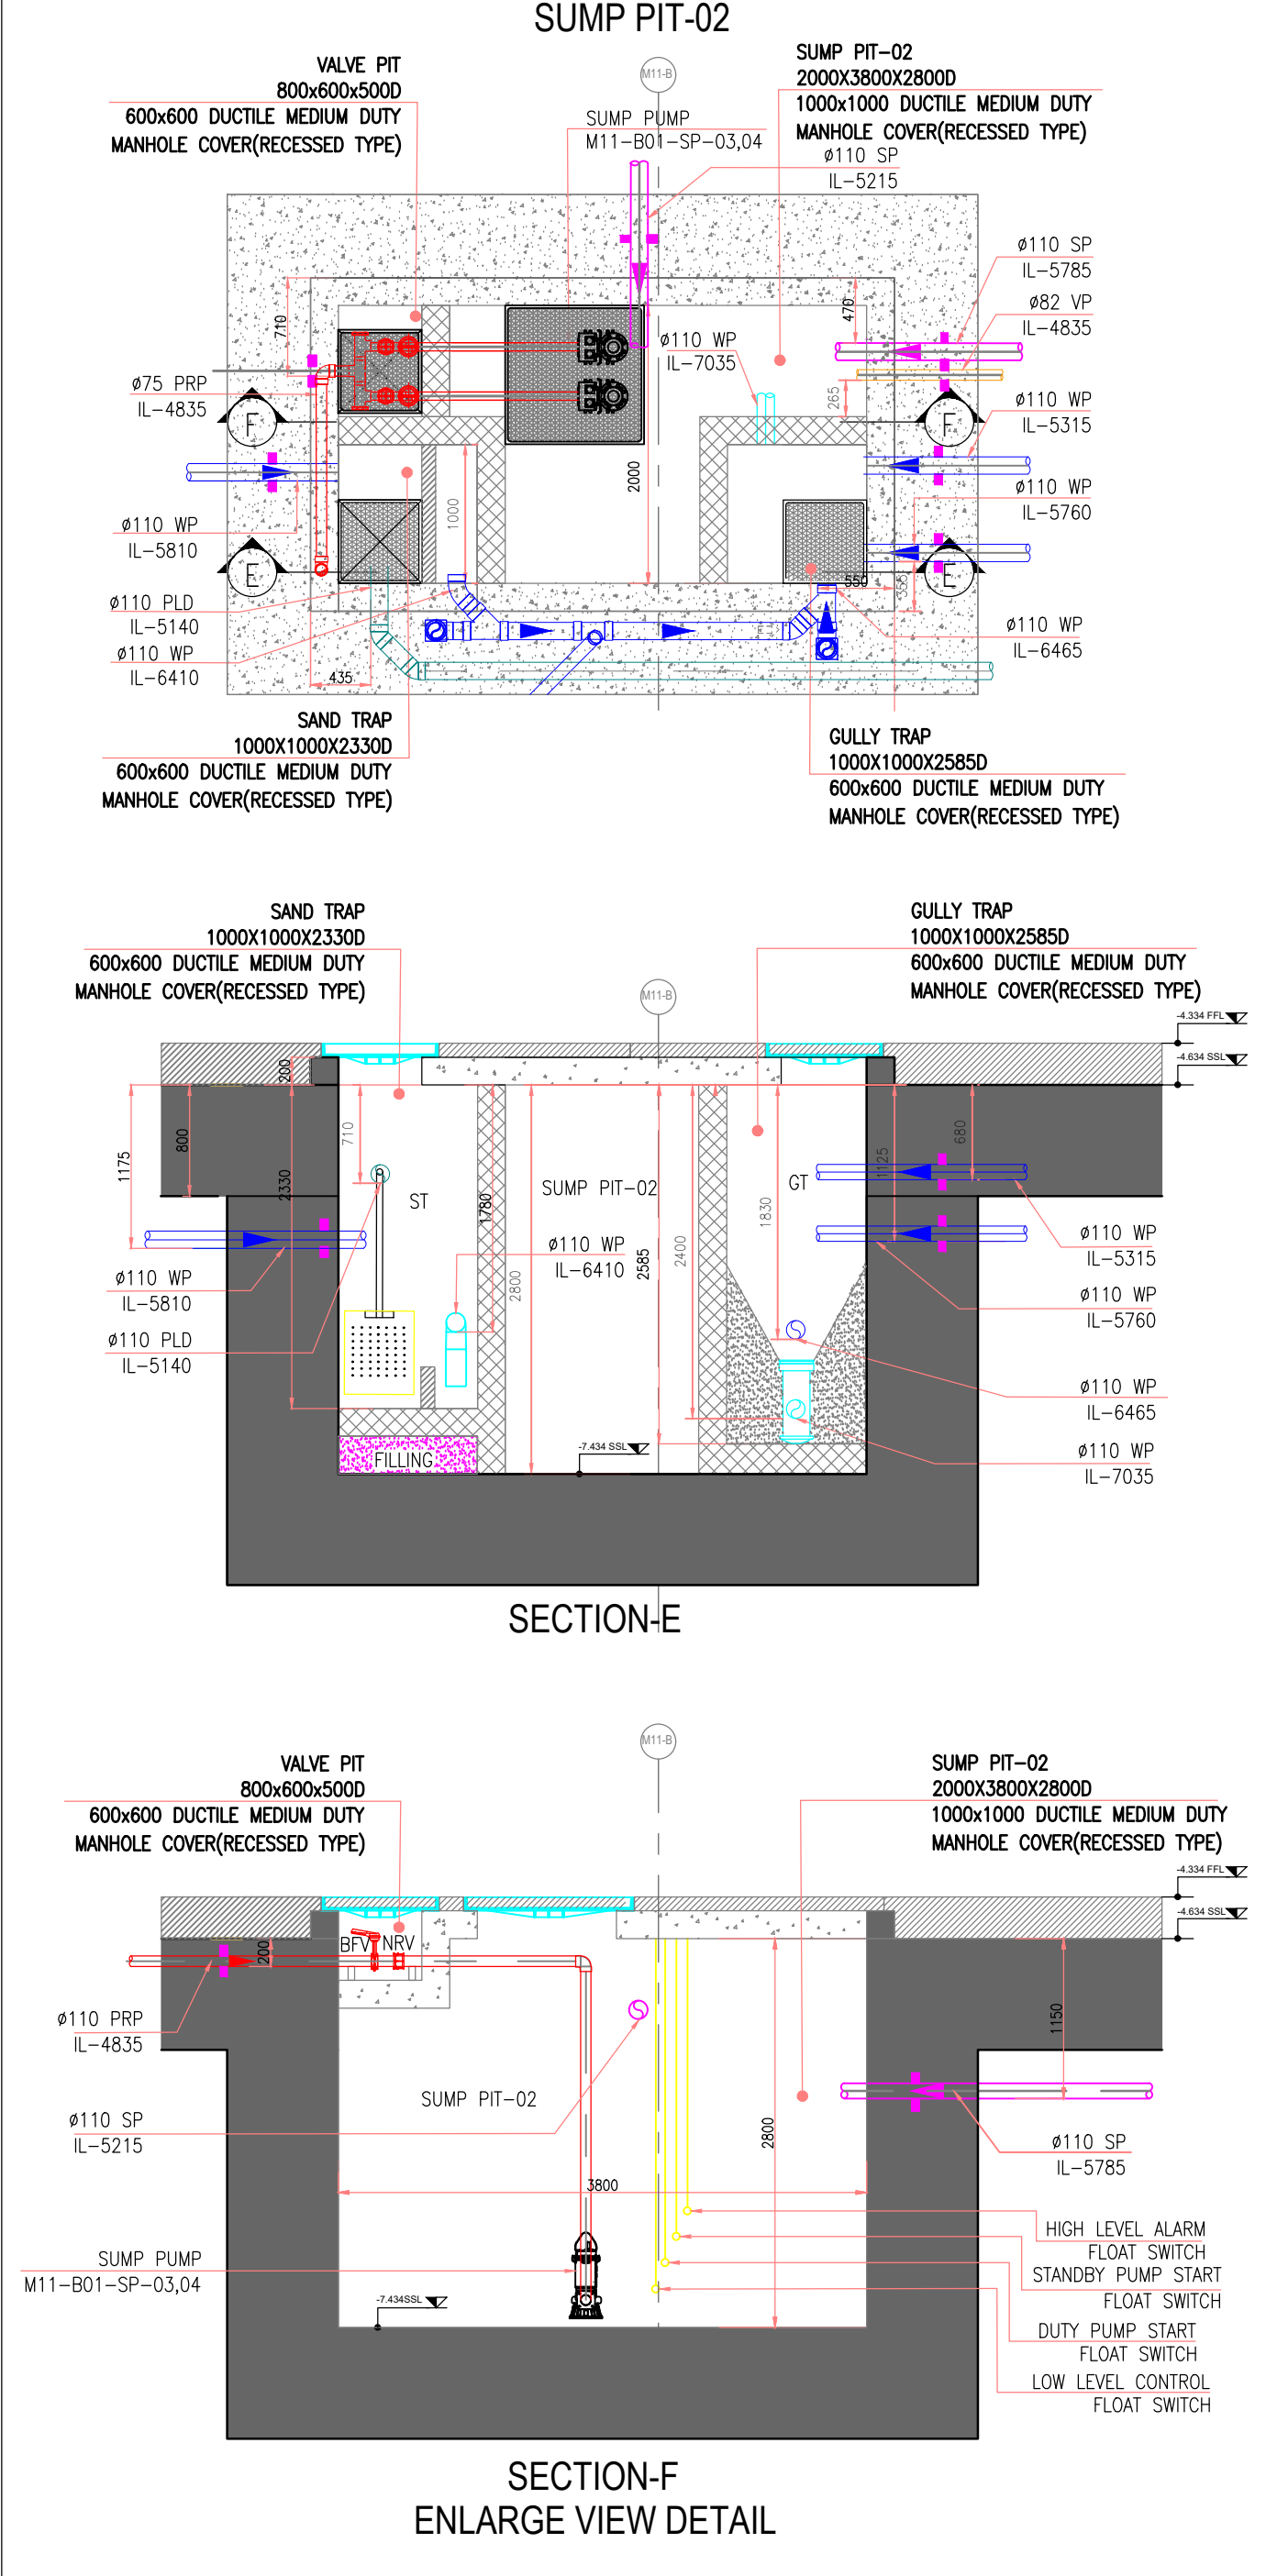


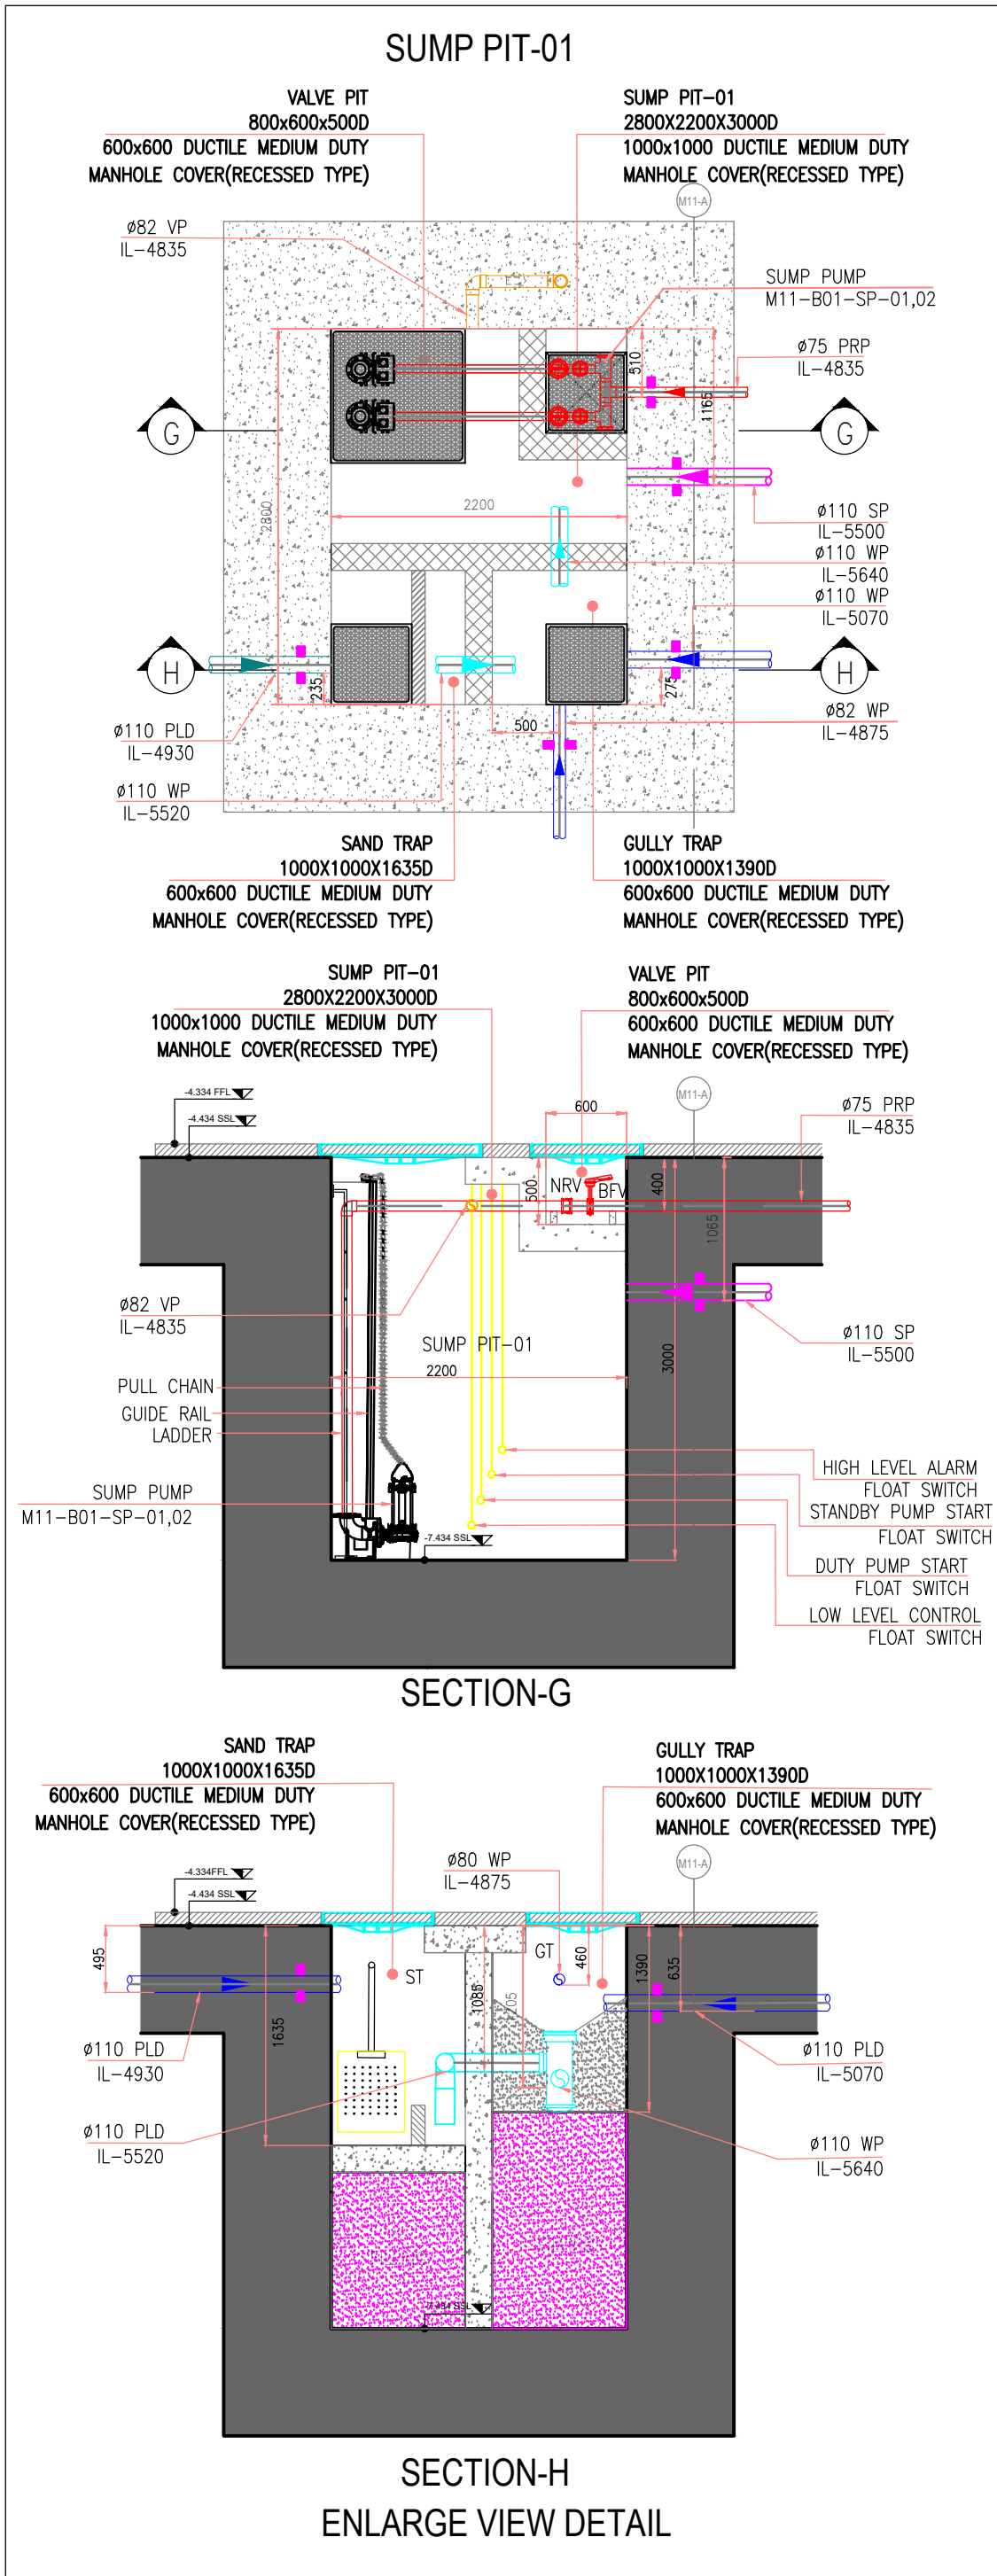

KEY PLAN:

Approval Stamp

Notes:

1. ALL DIMENSIONS AND LEVELS ARE IN MILLIMETERS
UNLESS OTHERWISE NOTED.

100% DD REFERENCE		
DRAWING NO.	DRAWING TITLE	REV
RST-RSP-M11-EV4-B01-DRW-ARC-220001	PLOT M11-BASEMENT FLOOR PLAN	P00
RST-RSP-M11-EV4-B01-DRW-STR-220001	FOUNDATION LEVEL GENERAL ARRANGEMENT	P00
RST-RSP-M11-EV4-B01-DRW-IDN-220001	OVERALL FLOOR PLAN - M11 EV AT BASEMENT FLOOR	P03
RST-RSP-M11-EV4-B01-DRW-LAN-110001	BASEMENT FLOOR - GENERAL ARRANGEMENT PLAN	P00
RST-RSP-M11-EV4-B01-DRW-PDR-220001	PLOT M11-BASEMENT FLOOR PLAN-DRAINAGE	P03

CITIC REVIEW STATUS :

REVIEWER	SIGN
ARCHITECT	
STRUCTURE	
ELECTRICAL	
MECHANICAL	
MEP-COORDINATOR	

REV. NO.	DATE	DESCRIPTION	APPRVD BY
01	23-07-2026	ISSUED FOR APPROVAL	SS
00	02-05-2026	ISSUED FOR APPROVAL	SS

Project:

KETURAH RESORT

Client:

مدينة دبي الطبية
Dubai Healthcare City

Developer:

مجموعة حياة
MAG OF LIFE
MAG OF LIFE FZ-LLC

Design Consultant:

Lead Consultant / Supervision Engineer:

RSP ARCHITECTS PLANNERS & ENGINEERS (P) LTD.
Dubai Branch
P.O. Box 437358, Dubai, U.A.E.
Tel: +971 4 610 1050
Fax: +971 4 610 6275
www.rsp.ae

RSP

Main Contractor:

中信建设（阿联酋）有限责任公司
CITIC MIDDLE EAST CONTRACTING LLC

M.E.P. Contractor:

中信建设（阿联酋）有限责任公司
CITIC MIDDLE EAST CONTRACTING LLC

Building Reference:

M11

Drawing Title:

**PLOT M11-BASEMENT FLOOR
PLAN-DRAINAGE**

Prepared	Noor	Checked	Siva
Drawn	Noor	Approved	Ahmed
Scale	NTS	Date	23-07-2026
Original Size	@A1	Project No.	

RST-CIT-M11-EV4-B01-DRW-PDR-220002 Rev. 01
Sheet 2 OF 3